Железнодорожный кран ЕДК-1000 г/п - 125 тс ГДР

Схема установки крана на аутригеры

Рабочее положение крана

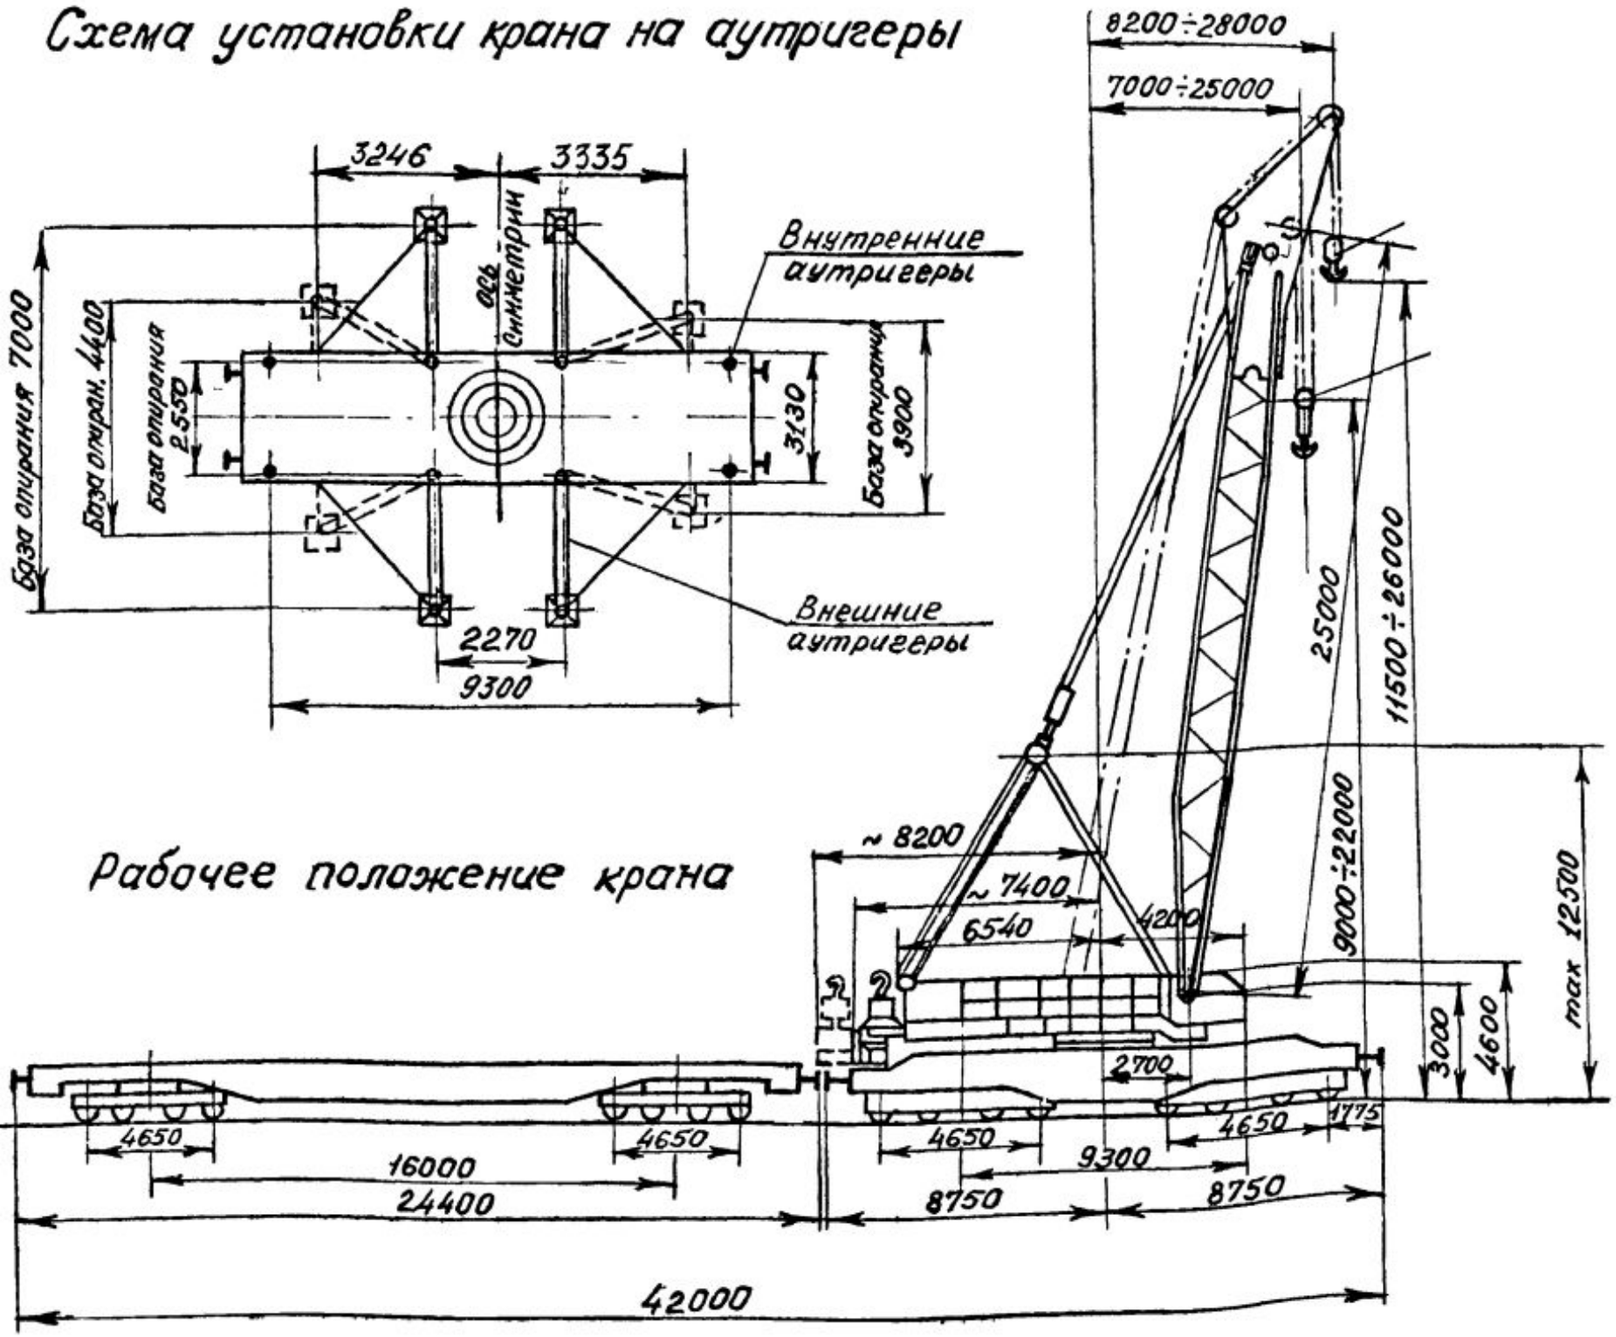

Высота подъема крюка у крана

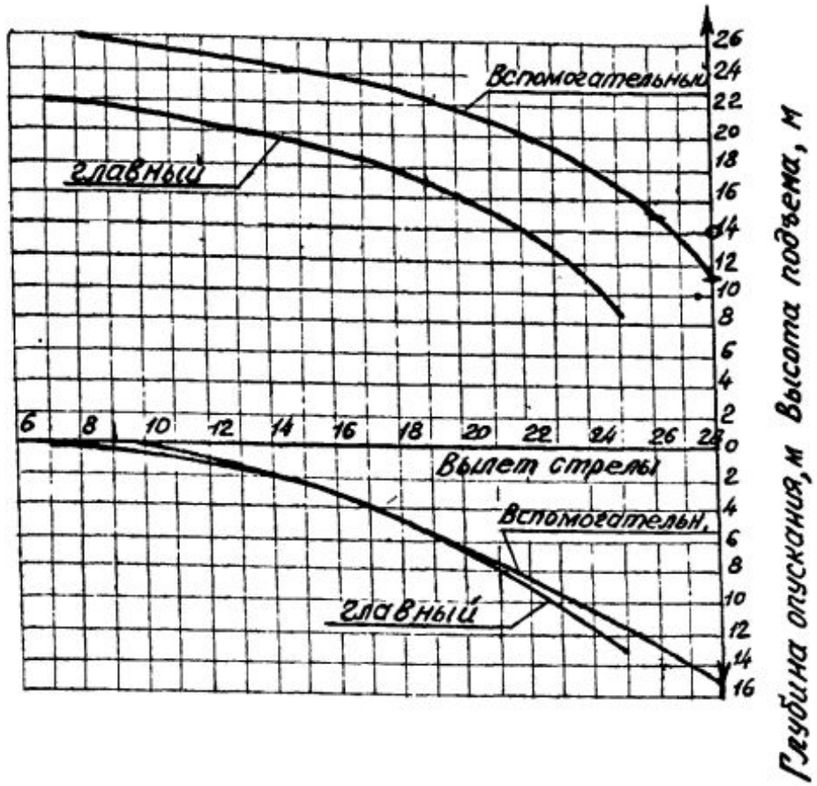

В условиях эксплуатируемых железных дорог применение кранов ЕДК-1000, находящихся в эксплуатации восстановительных поездов МПС, допустимо лишь при расстановке внешних аутригеров с максимальной базой 7м и обязательным использованием внутренних аутригеров крана.

Грузоподъемность крана при работе на аутригерах при опорной базе 7 м с поворотом 360°

На главном крюке (тс)				На вспомогательном крюке (тс)			
Вылет стрелы м	Число противовесов			Вылет стрелы м	Число противовесов		
	2	1	0		2	1	0
7	125	100	100	8 2	20	20	20
8	125	100	84	9.3	20	20	20
9	110	90	70	10.5	20	20	20
10	96	80	58	11.6	20	20	20
11	85	71	48	12.8	20	20	20
12	76	63	41	13.9	20	20	20
13	68	55	35	15.0	20	20	20
14	62	49	31	16.1	20	20	20
15	57	44	28	17.2	20	20	20
16	53	40	25	18.3	20	20	20
17	49	36	22	19.3	20	20	18
18	46	33	19	20.3	20	20	16
19	43	30	18	21.4	20	20	14.5
20	40	28	16	22.5	20	20	13
21	37	26	14	23.6	20	20	11.5
22	35	24	13	24.7	20	20	10.5
23	33	22	11	25.8	20	20	9.5
24	31	20	10	26.9	20	18	8.5
25	29	19	9	28.0	20	17	8

Техническая характеристика крана

NN пп	Наименование		Ед. изм.	Кол.
1	Максимальная грузоподъемность	на главном крюке	тс	125
		на вспомог. крюке	тс	20
2	Максимальная высота подъема крюка	главного	м	22
		вспомогательного	м	26
3	Скорость подъема главного крюка	с нагрузкой до 40 тс	м/мин	~4
		с нагрузкой до 125 тс	м/мин	~2
4	Скорость движения самоходом		км/час	6.0
5	Масса крана в рабочем положении	с 2 противовесами	тс	222
		без противовесов	тс	170
6	Количество аутригеров внешних		шт.	4
7	Количество аутригеров внутренних		шт.	4